La maison de vos rêves, commence par un bon plan...

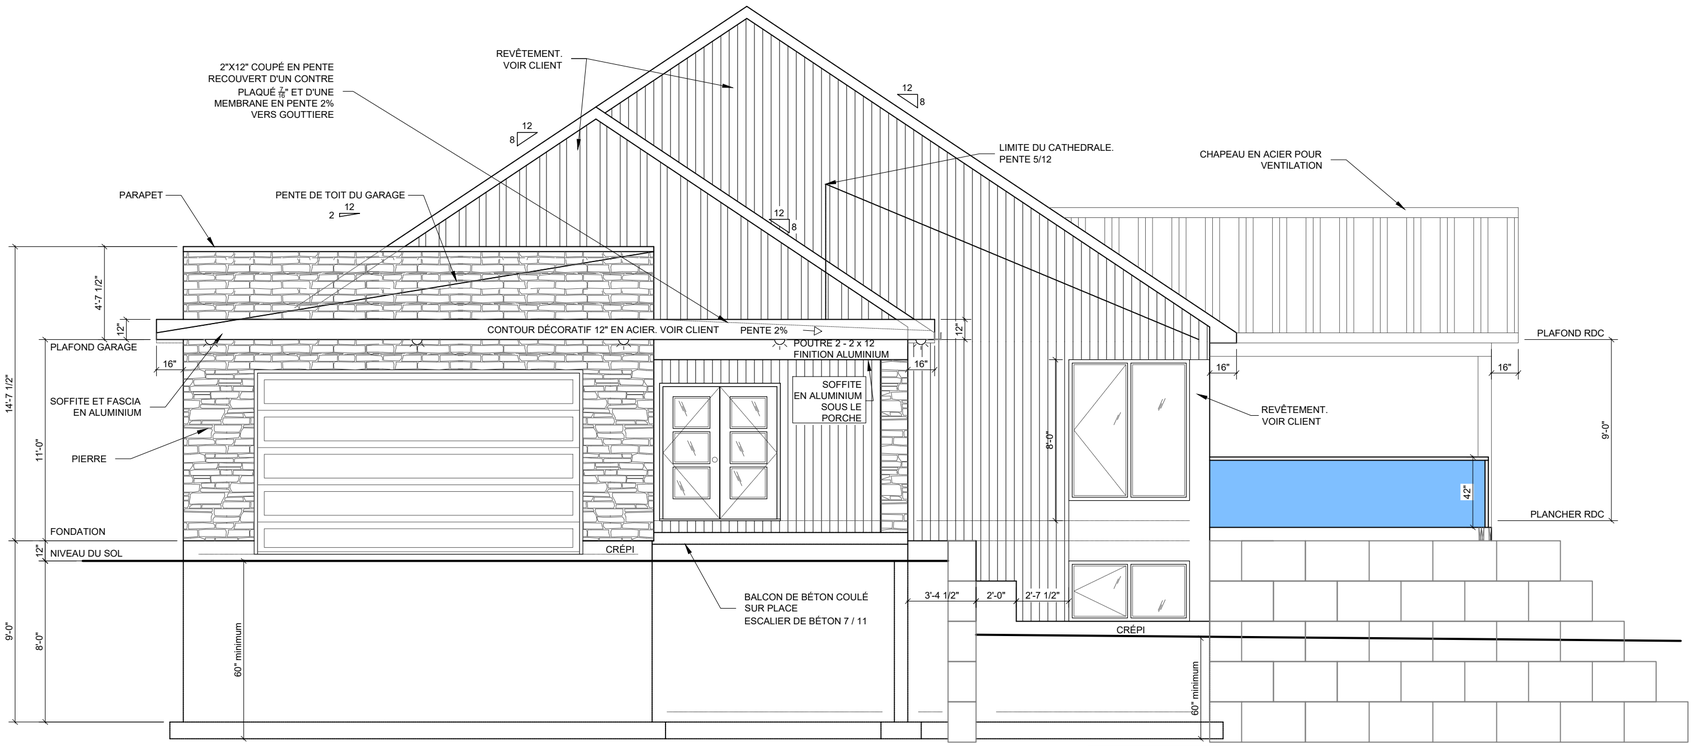

RDC:	1661pi²
TOTAL:	1661 pi²
GARAGE:	600 pi²

AVANT

echelle: 3/16"=1'-0"

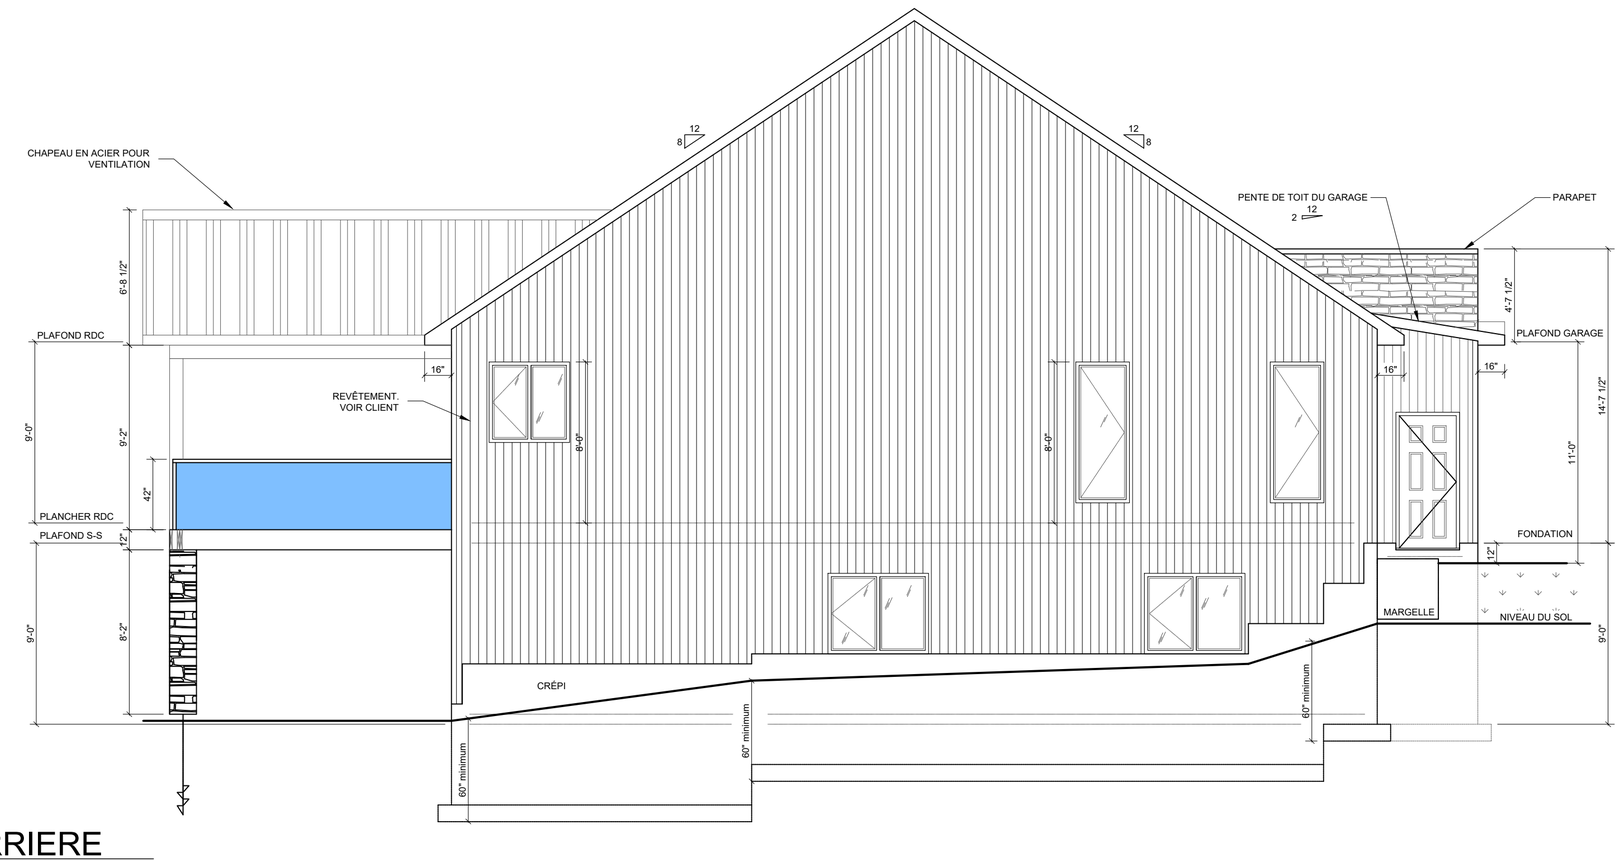

ARRIERE

echelle: 3/16"=1'-0"

NOTES :

L'ENTREPRENEUR DOIT S'ASSURER AUPRÈS DE SON CLIENT QUE LES PLANS RÉPONDENT ADÉQUATEMENT AUX RÈGLEMENTS MUNICIPAUX OÙ AURA LIEU LA CONSTRUCTION. LE CLIENT A LA RESPONSABILITÉ DE VÉRIFIER LES NORMES AUPRÈS DE SA MUNICIPALITÉ. CEUX-CI VARIENT SELON LES RÉGIONS ET PEUVENT NÉCESSITER DES CHANGEMENTS AUX PLANS.

L'ORIGINAL DE CE PLAN À ÉTÉ DESSINÉ PAR UN TECHNICIEN ET EN EST SA PROPRIÉTÉ EXCLUSIVE. TOUTE REPRODUCTION DE LA PRÉSENTE COPIE PAR QUELQUE MOYEN QUE CE SOIT EST STRICTEMENT INTERDITE.

L'ACHAT DE CE PLAN DE MAISON NE VOUS PERMET PAS D'UTILISER CE MODÈLE À DES FINS PUBLICITAIRES. À MOINS D'OBTENIR PRÉALABLEMENT UNE LICENCE À CET EFFET.

LA CONSTRUCTION DE PLUS D'UNE MAISON À PARTIR DES PLANS DE CE MODÈLE NÉCESSITE OBLIGATOIREMENT L'OBTENTION D'UNE LICENCE.

NOTES IMPORTANTES:

DONNÉES FOURNIES POUR DES CONDITIONS "STANDARDS". LES NORMES DU CODE NATIONAL SONT APPLICABLES. L'ENTREPRENEUR ET/OU LES SOUS-TRAITANTS DOIVENT VÉRIFIER TOUTES LES DONNÉES AVANT LE DÉBUT DES TRAVAUX, S'ASSURER DE LA CONFORMITÉ AVEC LES CODES APPLICABLES ET VÉRIFIER LES CONDITIONS SUR LE TERRAIN. AUCUNE DIMENSION NE DOIT ÊTRE MESURÉE À L'ÉCHELLE SUR LES PLANS.

RÉVISION	%	DATE	PAR
FINALE	100%	15/09/2023	M.V.
PRÉLIMINAIRE	99%	07/09/2023	M.V.
PRÉLIMINAIRE	66%	05/09/2023	M.V.
PRÉLIMINAIRE	33%	31/08/2023	M.V.

VÉRIFIÉ: M.V.

CONCU: P.H.

RÉALISÉ: P.H.

CLIENT: YAN ET LAU

PROJET: Residence Principale

DESSIN: AVANT & ARRIERE

DATE: 13/09/2023

NO. FEUILLE: 1/6

PROJET NO: C-23-008

La maison de vos rêves, commence par un bon plan...

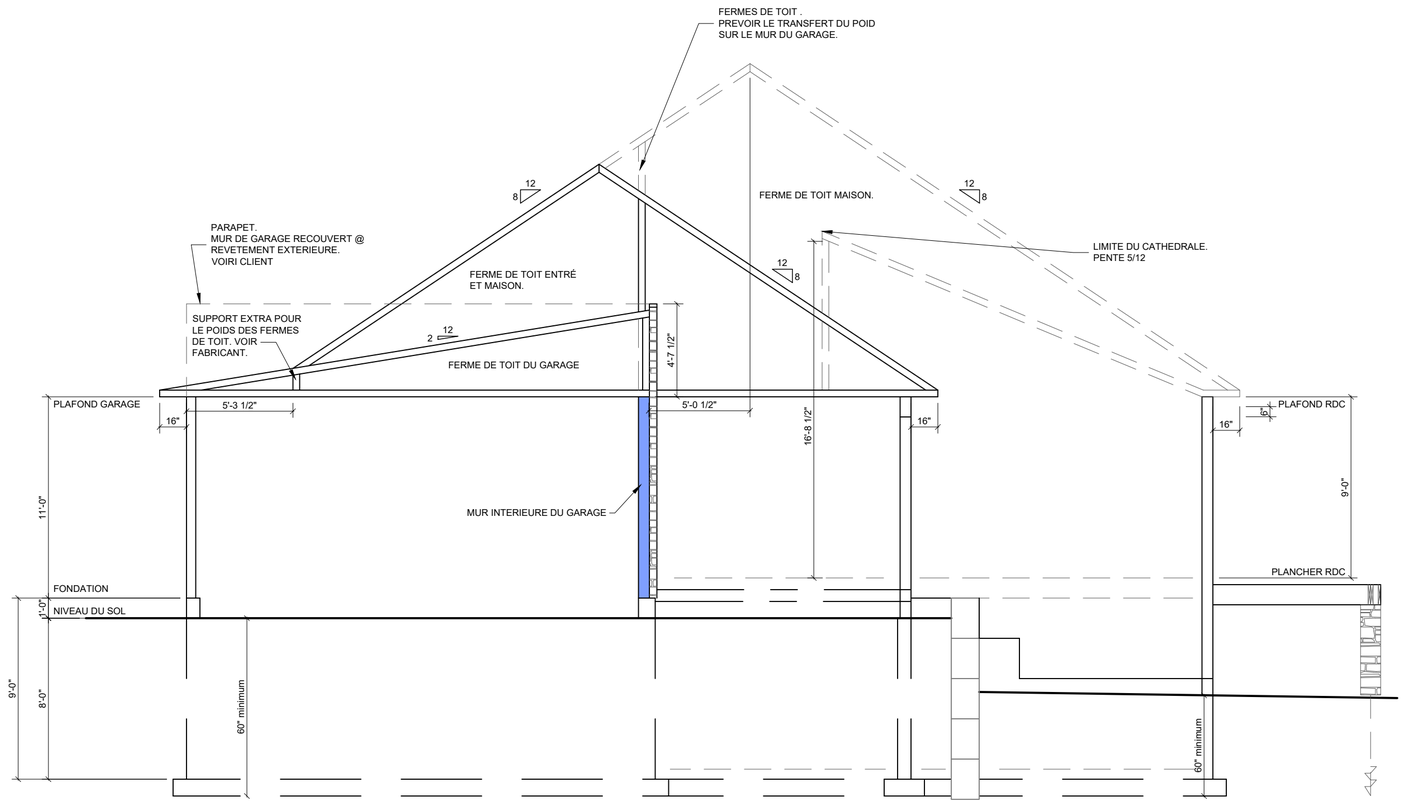

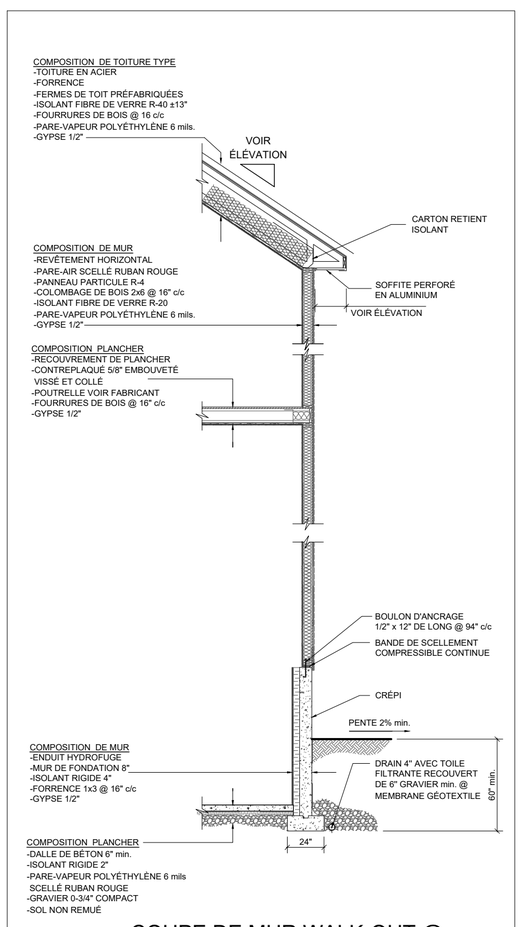

COUPE DE MUR WALK-OUT @ REVETEMENT HORIZONTAL

ÉCHELLE: N.A.E.

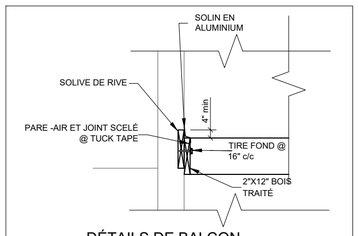

DÉTAILS DE BALCON

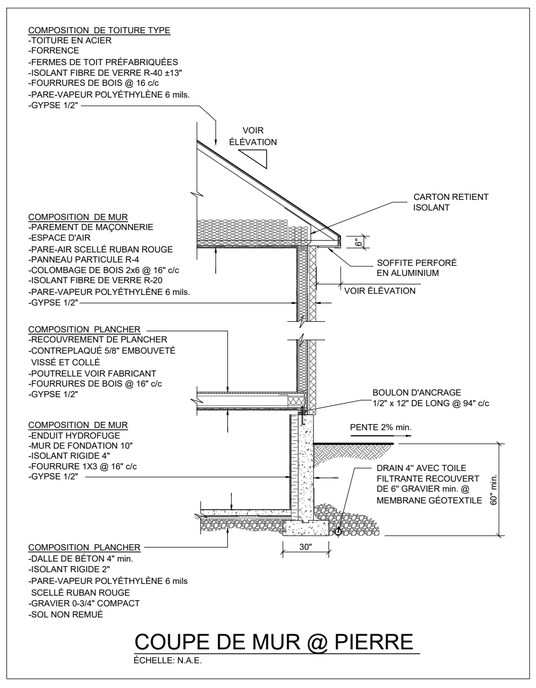

COUPE DE MUR @ PIERRE

ÉCHELLE: N.A.E.

NOTES :

L'ENTREPRENEUR DOIT S'ASSURER AUPRÈS DE SON CLIENT QUE LES PLANS RÉPONDENT ADÉQUATEMENT AUX RÈGLEMENTS MUNICIPAUX OÙ AURA LIEU LA CONSTRUCTION. LE CLIENT A LA RESPONSABILITÉ DE VÉRIFIER LES NORMES AUPRÈS DE SA MUNICIPALITÉ. CEUX-CI VARIENT SELON LES RÉGIONS ET PEUVENT NÉCESSITER DES CHANGEMENTS AUX PLANS.

L'ORIGINAL DE CE PLAN À ÉTÉ DESSINÉ PAR UN TECHNICIEN ET EN EST SA PROPRIÉTÉ EXCLUSIVE. TOUTE REPRODUCTION DE LA PRÉSENTE COPIE PAR QUELQUE MOYEN QUE CE SOIT EST STRICTEMENT INTERDITE.

L'ACHAT DE CE PLAN DE MAISON NE VOUS PERMET PAS D'UTILISER CE MODÈLE À DES FINS PUBLICITAIRES. À MOINS D'OBTENIR PRÉALABLEMENT UNE LICENCE À CET EFFET.

LA CONSTRUCTION DE PLUS D'UNE MAISON À PARTIR DES PLANS DE CE MODÈLE NÉCESSITE OBLIGATOIREMENT L'OBTENTION D'UNE LICENCE.

NOTES IMPORTANTES:

DONNÉES FOURNIES POUR DES CONDITIONS "STANDARDS". LES NORMES DU CODE NATIONAL SONT APPLICABLES. L'ENTREPRENEUR ET/OU LES SOUS-TRAITANTS DOIVENT VÉRIFIER TOUTES LES DONNÉES AVANT LE DÉBUT DES TRAVAUX, S'ASSURER DE LA CONFORMITÉ AVEC LES CODES APPLICABLES ET VÉRIFIER LES CONDITIONS SUR LE TERRAIN. AUCUNE DIMENSION NE DOIT ÊTRE MESURÉE À L'ÉCHELLE SUR LES PLANS.

RÉVISION	%	DATE	PAR
FINALE	100%	15/09/2023	M.V.
PRÉLIMINAIRE	99%	07/09/2023	M.V.
PRÉLIMINAIRE	66%	05/09/2023	M.V.
PRÉLIMINAIRE	33%	31/08/2023	M.V.

VÉRIFIÉ: M.V.

CONCU: P.H.

RÉALISÉ: P.H.

CLIENT: YAN ET LAU

PROJET: Residence Principale

DESSIN: COUPE & DETAILS

DATE: 13/09/2023

NO. FEUILLE: 6/6

PROJET NO: C-23-008

La maison de vos rêves, commence par un bon plan...

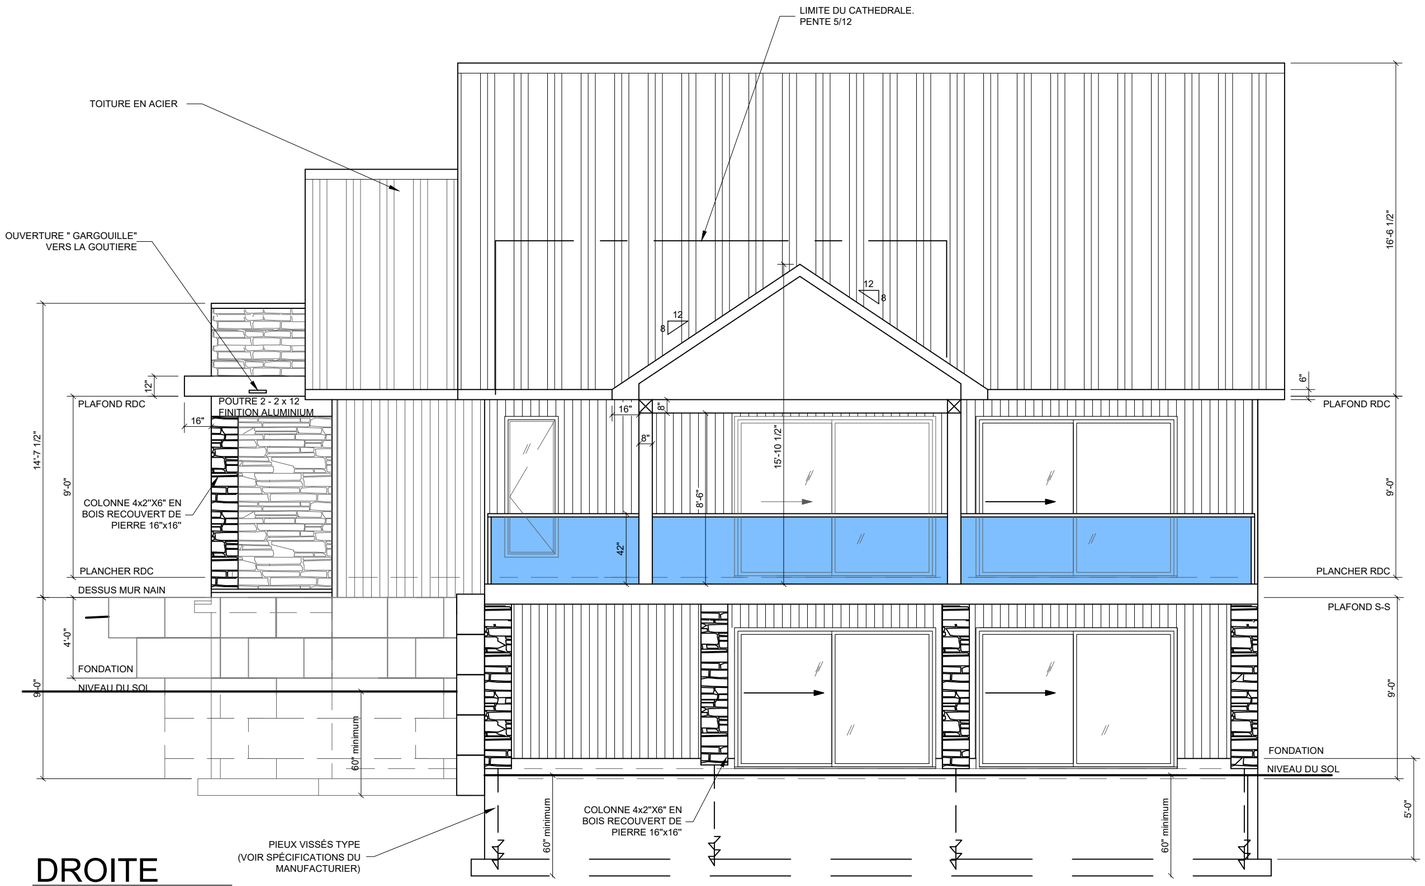

DROITE

echelle: 3/16"=1'-0"

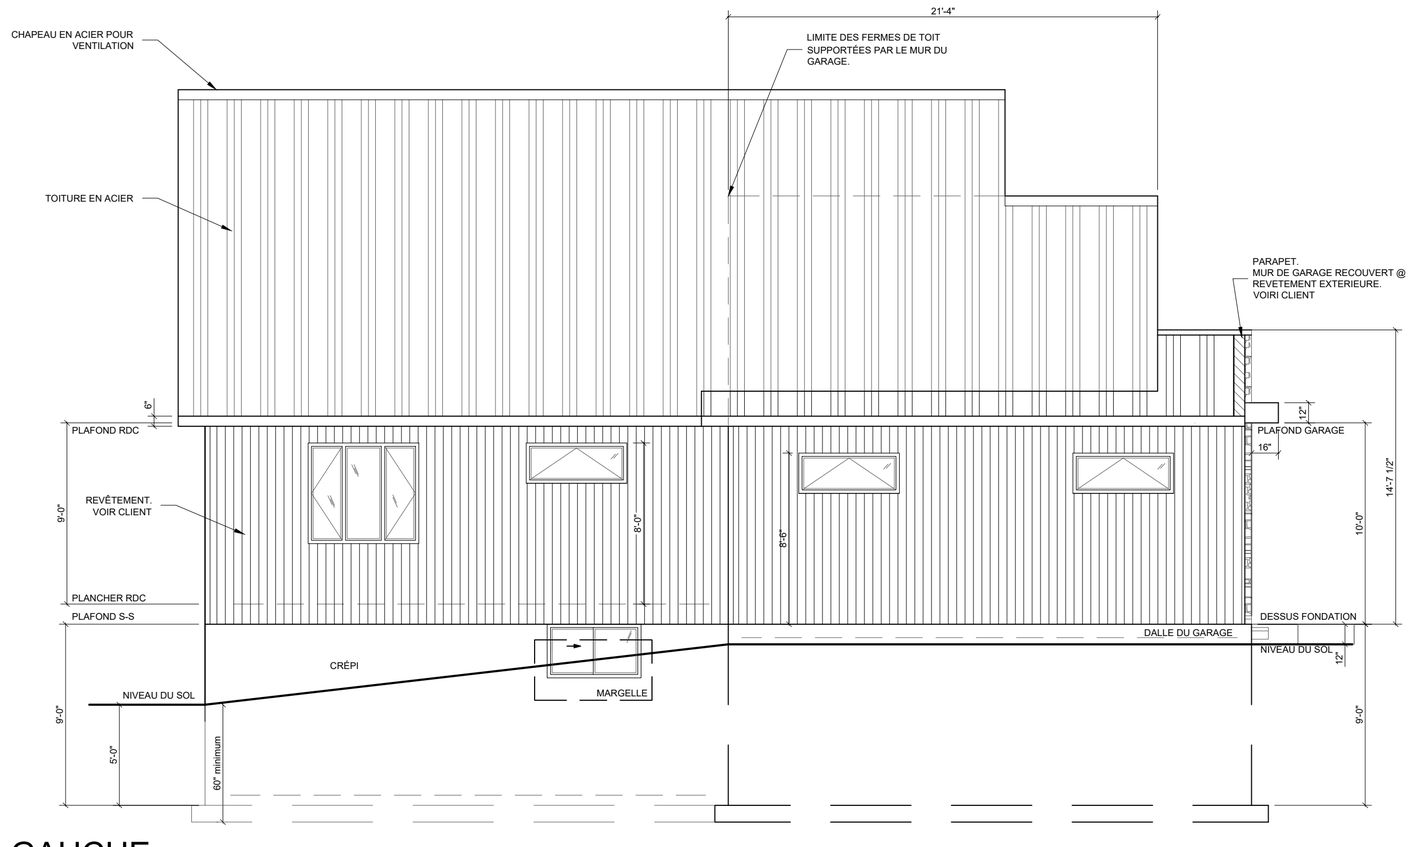

GAUCHE

echelle: 3/16"=1'-0"

NOTES :

L'ENTREPRENEUR DOIT S'ASSURER AUPRÈS DE SON CLIENT QUE LES PLANS RÉPONDENT ADÉQUATEMENT AUX RÈGLEMENTS MUNICIPAUX OÙ AURA LIEU LA CONSTRUCTION. LE CLIENT A LA RESPONSABILITÉ DE VÉRIFIER LES NORMES AUPRÈS DE SA MUNICIPALITÉ. CEUX-CI VARIENT SELON LES RÉGIONS ET PEUVENT NÉCESSITER DES CHANGEMENTS AUX PLANS.

L'ORIGINAL DE CE PLAN À ÉTÉ DESSINÉ PAR UN TECHNICIEN ET EN EST SA PROPRIÉTÉ EXCLUSIVE. TOUTE REPRODUCTION DE LA PRÉSENTE COPIE PAR QUELQUE MOYEN QUE CE SOIT EST STRICTEMENT INTERDITE.

L'ACHAT DE CE PLAN DE MAISON NE VOUS PERMET PAS D'UTILISER CE MODÈLE À DES FINS PUBLICITAIRES, À MOINS D'OBTENIR PRÉALABLEMENT UNE LICENCE À CET EFFET.

LA CONSTRUCTION DE PLUS D'UNE MAISON À PARTIR DES PLANS DE CE MODÈLE NÉCESSITE OBLIGATOIREMENT L'OBTENTION D'UNE LICENCE.

NOTES IMPORTANTES:

DONNÉES FOURNIES POUR DES CONDITIONS "STANDARDS". LES NORMES DU CODE NATIONAL SONT APPLICABLES. L'ENTREPRENEUR ET/OU LES SOUS-TRAITANTS DOIVENT VÉRIFIER TOUTES LES DONNÉES AVANT LE DÉBUT DES TRAVAUX, S'ASSURER DE LA CONFORMITÉ AVEC LES CODES APPLICABLES ET VÉRIFIER LES CONDITIONS SUR LE TERRAIN. AUCUNE DIMENSION NE DOIT ÊTRE MESURÉE À L'ÉCHELLE SUR LES PLANS.

RÉVISION	%	DATE	PAR
FINALE	100%	15/09/2023	M.V.
PRÉLIMINAIRE	99%	07/09/2023	M.V.
PRÉLIMINAIRE	66%	05/09/2023	M.V.
PRÉLIMINAIRE	33%	31/08/2023	M.V.

VÉRIFIÉ: M.V.

CONCU: P.H.

RÉALISÉ: P.H.

CLIENT: YAN ET LAU

PROJET: Residence Principale

DESSIN: DROITE & GAUCHE

DATE: 13/09/2023

NO. FEUILLE: 2/6

PROJET NO: C-23-008

La maison de vos rêves, commence par un bon plan...

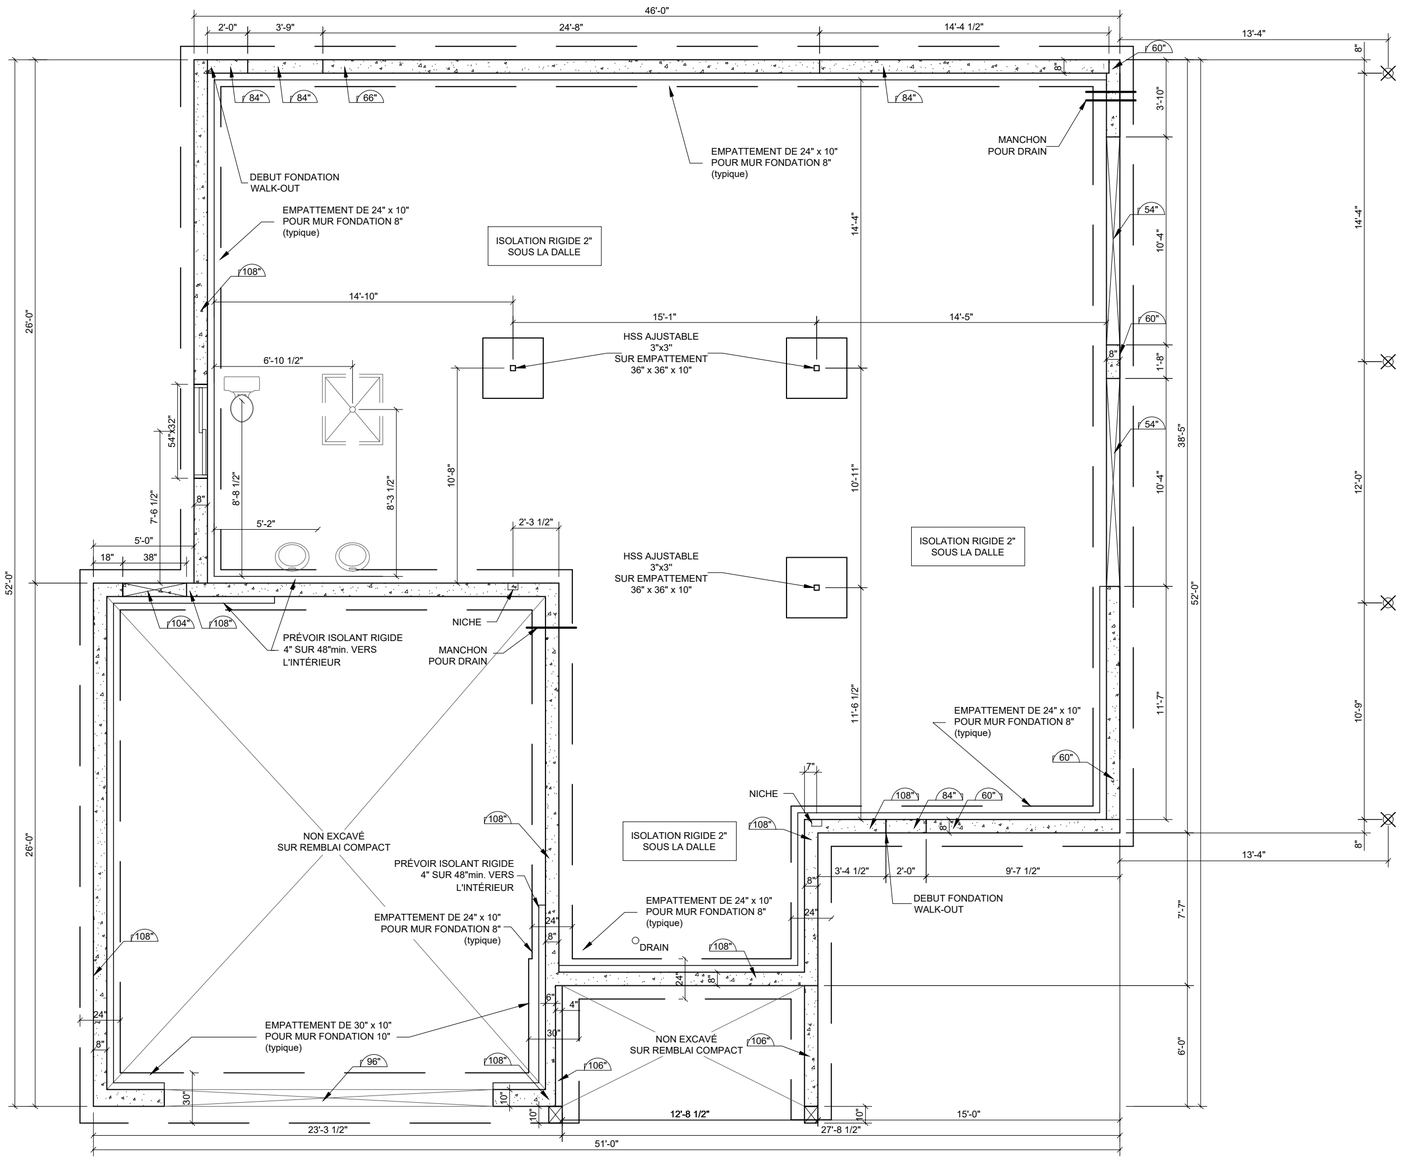

FONDATION

echelle: 3/16"=1'-0"

NOTES :

L'ENTREPRENEUR DOIT S'ASSURER AUPRÈS DE SON CLIENT QUE LES PLANS RÉPONDENT ADÉQUATEMENT AUX RÈGLEMENTS MUNICIPAUX OÙ AURA LIEU LA CONSTRUCTION. LE CLIENT A LA RESPONSABILITÉ DE VÉRIFIER LES NORMES AUPRÈS DE SA MUNICIPALITÉ. CEUX-CI VARIENT SELON LES RÉGIONS ET PEUVENT NÉCESSITER DES CHANGEMENTS AUX PLANS.

L'ORIGINAL DE CE PLAN À ÉTÉ DESSINÉ PAR UN TECHNICIEN ET EN EST SA PROPRIÉTÉ EXCLUSIVE. TOUTE REPRODUCTION DE LA PRÉSENTE COPIE PAR QUELQUE MOYEN QUE CE SOIT EST STRICTEMENT INTERDITE.

L'ACHAT DE CE PLAN DE MAISON NE VOUS PERMET PAS D'UTILISER CE MODÈLE À DES FINS PUBLICITAIRES, À MOINS D'OBTENIR PRÉALABLEMENT UNE LICENCE À CET EFFET.

LA CONSTRUCTION DE PLUS D'UNE MAISON À PARTIR DES PLANS DE CE MODÈLE NÉCESSITE OBLIGATOIREMENT L'OBTENTION D'UNE LICENCE.

NOTES IMPORTANTES:

DONNÉES FOURNIES POUR DES CONDITIONS "STANDARDS". LES NORMES DU CODE NATIONAL SONT APPLICABLES. L'ENTREPRENEUR ET/OU LES SOUS-TRAITANTS DOIVENT VÉRIFIER TOUTES LES DONNÉES AVANT LE DÉBUT DES TRAVAUX, S'ASSURER DE LA CONFORMITÉ AVEC LES CODES APPLICABLES ET VÉRIFIER LES CONDITIONS SUR LE TERRAIN. AUCUNE DIMENSION NE DOIT ÊTRE MESURÉE À L'ÉCHELLE SUR LES PLANS.

RÉVISION	%	DATE	PAR
FINALE	100%	15/09/2023	M.V.
PRÉLIMINAIRE	99%	07/09/2023	M.V.
PRÉLIMINAIRE	66%	05/09/2023	M.V.
PRÉLIMINAIRE	33%	31/08/2023	M.V.

VÉRIFIÉ: M.V.

CONCU: P.H.

RÉALISÉ: P.H.

CLIENT: YAN ET LAU

PROJET: Residence Principale

DESSIN: FONDATION

DATE: 13/09/2023

NO. FEUILLE: 3/6

PROJET NO: C-23-008

La maison de vos rêves, commence par un bon plan...

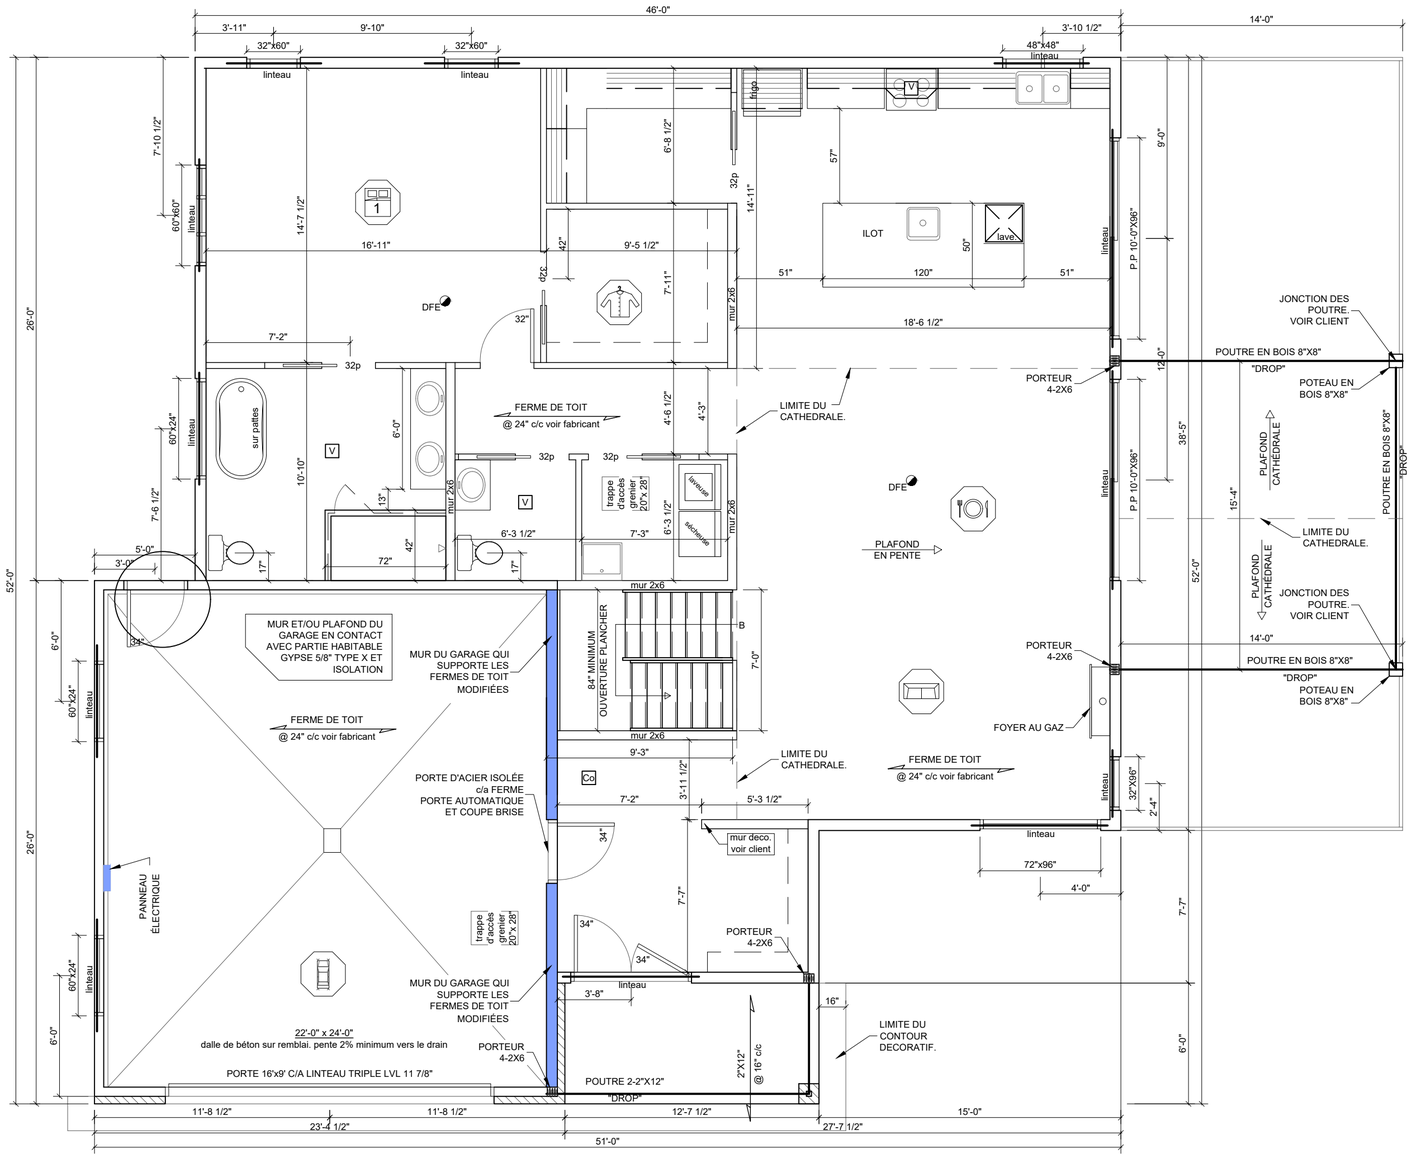

RDC

echelle: 3/16"=1'-0"

NOTES :

L'ENTREPRENEUR DOIT S'ASSURER AUPRÈS DE SON CLIENT QUE LES PLANS RÉPONDENT ADÉQUATEMENT AUX RÈGLEMENTS MUNICIPAUX OÙ AURA LIEU LA CONSTRUCTION. LE CLIENT A LA RESPONSABILITÉ DE VÉRIFIER LES NORMES AUPRÈS DE SA MUNICIPALITÉ. CEUX-CI VARIENT SELON LES RÉGIONS ET PEUVENT NÉCESSITER DES CHANGEMENTS AUX PLANS.

L'ORIGINAL DE CE PLAN À ÉTÉ DESSINÉ PAR UN TECHNICIEN ET EN EST SA PROPRIÉTÉ EXCLUSIVE. TOUTE REPRODUCTION DE LA PRÉSENTE COPIE PAR QUELQUE MOYEN QUE CE SOIT EST STRICTEMENT INTERDITE.

L'ACHAT DE CE PLAN DE MAISON NE VOUS PERMET PAS D'UTILISER CE MODÈLE À DES FINS PUBLICITAIRES. À MOINS D'OBTENIR PRÉALABLEMENT UNE LICENCE À CET EFFET.

LA CONSTRUCTION DE PLUS D'UNE MAISON À PARTIR DES PLANS DE CE MODÈLE NÉCESSITE OBLIGATOIREMENT L'OBTENTION D'UNE LICENCE.

NOTES IMPORTANTES:

DONNÉES FOURNIES POUR DES CONDITIONS "STANDARDS". LES NORMES DU CODE NATIONAL SONT APPLICABLES. L'ENTREPRENEUR ET/OU LES SOUS-TRAITANTS DOIVENT VÉRIFIER TOUTES LES DONNÉES AVANT LE DÉBUT DES TRAVAUX, S'ASSURER DE LA CONFORMITÉ AVEC LES CODES APPLICABLES ET VÉRIFIER LES CONDITIONS SUR LE TERRAIN. AUCUNE DIMENSION NE DOIT ÊTRE MESURÉE À L'ÉCHELLE SUR LES PLANS.

RÉVISION	%	DATE	PAR
FINALE	100%	15/09/2023	M.V.
PRÉLIMINAIRE	99%	07/09/2023	M.V.
PRÉLIMINAIRE	66%	05/09/2023	M.V.
PRÉLIMINAIRE	33%	31/08/2023	M.V.

VÉRIFIÉ: M.V.

CONCU: P.H.

RÉALISÉ: P.H.

CLIENT: YAN ET LAU

PROJET: Residence Principale

DESSIN: RDC

DATE: 13/09/2023

PROJET NO: C-23-008

NO. FEUILLE: 5/6

La maison de vos rêves, commence par un bon plan...

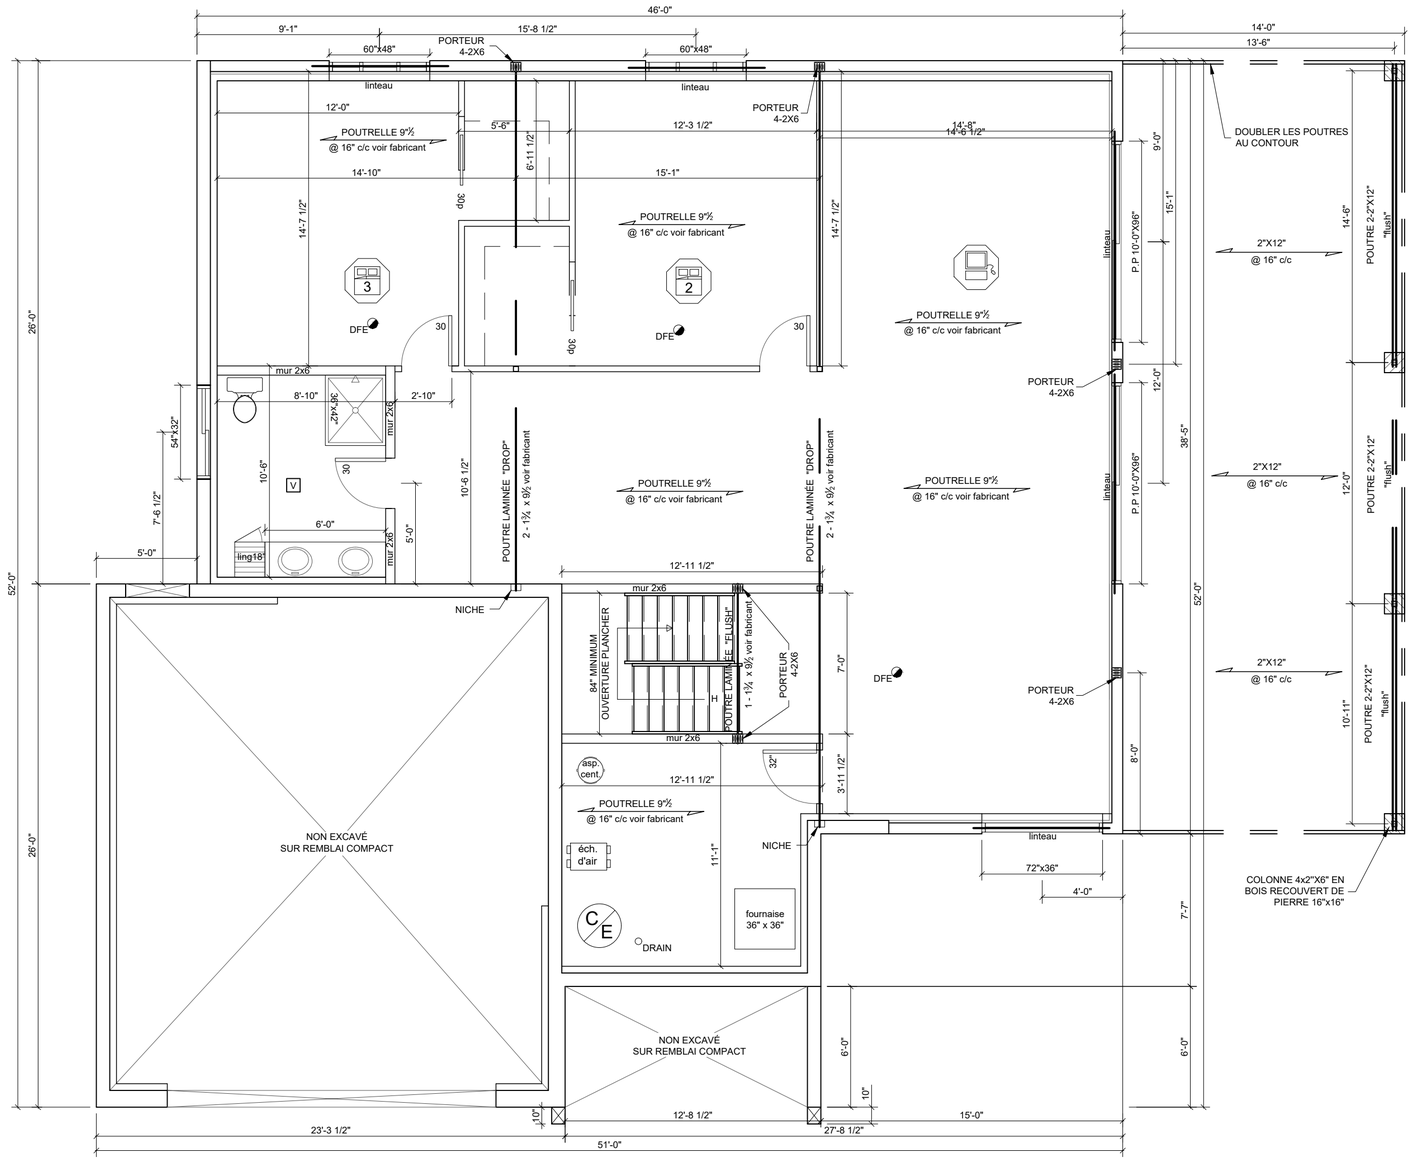

SOUS-SOL

echelle: 3/16"=1'-0"

NOTES :

L'ENTREPRENEUR DOIT S'ASSURER AUPRÈS DE SON CLIENT QUE LES PLANS RÉPONDENT ADÉQUATEMENT AUX RÈGLEMENTS MUNICIPAUX OÙ AURA LIEU LA CONSTRUCTION. LE CLIENT A LA RESPONSABILITÉ DE VÉRIFIER LES NORMES AUPRÈS DE SA MUNICIPALITÉ. CEUX-CI VARIENT SELON LES RÉGIONS ET PEUVENT NÉCESSITER DES CHANGEMENTS AUX PLANS.

L'ORIGINAL DE CE PLAN À ÉTÉ DESSINÉ PAR UN TECHNICIEN ET EN EST SA PROPRIÉTÉ EXCLUSIVE. TOUTE REPRODUCTION DE LA PRÉSENTE COPIE PAR QUELQUE MOYEN QUE CE SOIT EST STRICTEMENT INTERDITE.

L'ACHAT DE CE PLAN DE MAISON NE VOUS PERMET PAS D'UTILISER CE MODÈLE À DES FINS PUBLICITAIRES, À MOINS D'OBTENIR PRÉALABLEMENT UNE LICENCE À CET EFFET.

LA CONSTRUCTION DE PLUS D'UNE MAISON À PARTIR DES PLANS DE CE MODÈLE NÉCESSITE OBLIGATOIREMENT L'OBTENTION D'UNE LICENCE.

NOTES IMPORTANTES:

DONNÉES FOURNIES POUR DES CONDITIONS "STANDARDS". LES NORMES DU CODE NATIONAL SONT APPLICABLES. L'ENTREPRENEUR ET/OU LES SOUS-TRAITANTS DOIVENT VÉRIFIER TOUTES LES DONNÉES AVANT LE DÉBUT DES TRAVAUX, S'ASSURER DE LA CONFORMITÉ AVEC LES CODES APPLICABLES ET VÉRIFIER LES CONDITIONS SUR LE TERRAIN. AUCUNE DIMENSION NE DOIT ÊTRE MESURÉE À L'ÉCHELLE SUR LES PLANS.

RÉVISION	%	DATE	PAR
FINALE	100%	15/09/2023	M.V.
PRÉLIMINAIRE	99%	07/09/2023	M.V.
PRÉLIMINAIRE	66%	05/09/2023	M.V.
PRÉLIMINAIRE	33%	31/08/2023	M.V.

VÉRIFIÉ: M.V.

CONCU: P.H.

RÉALISÉ: P.H.

CLIENT: YAN ET LAU

PROJET: Residence Principale

DESSIN: SOUS-SOL

DATE: 13/09/2023

NO. FEUILLE: 4/6

PROJET NO: C-23-008